


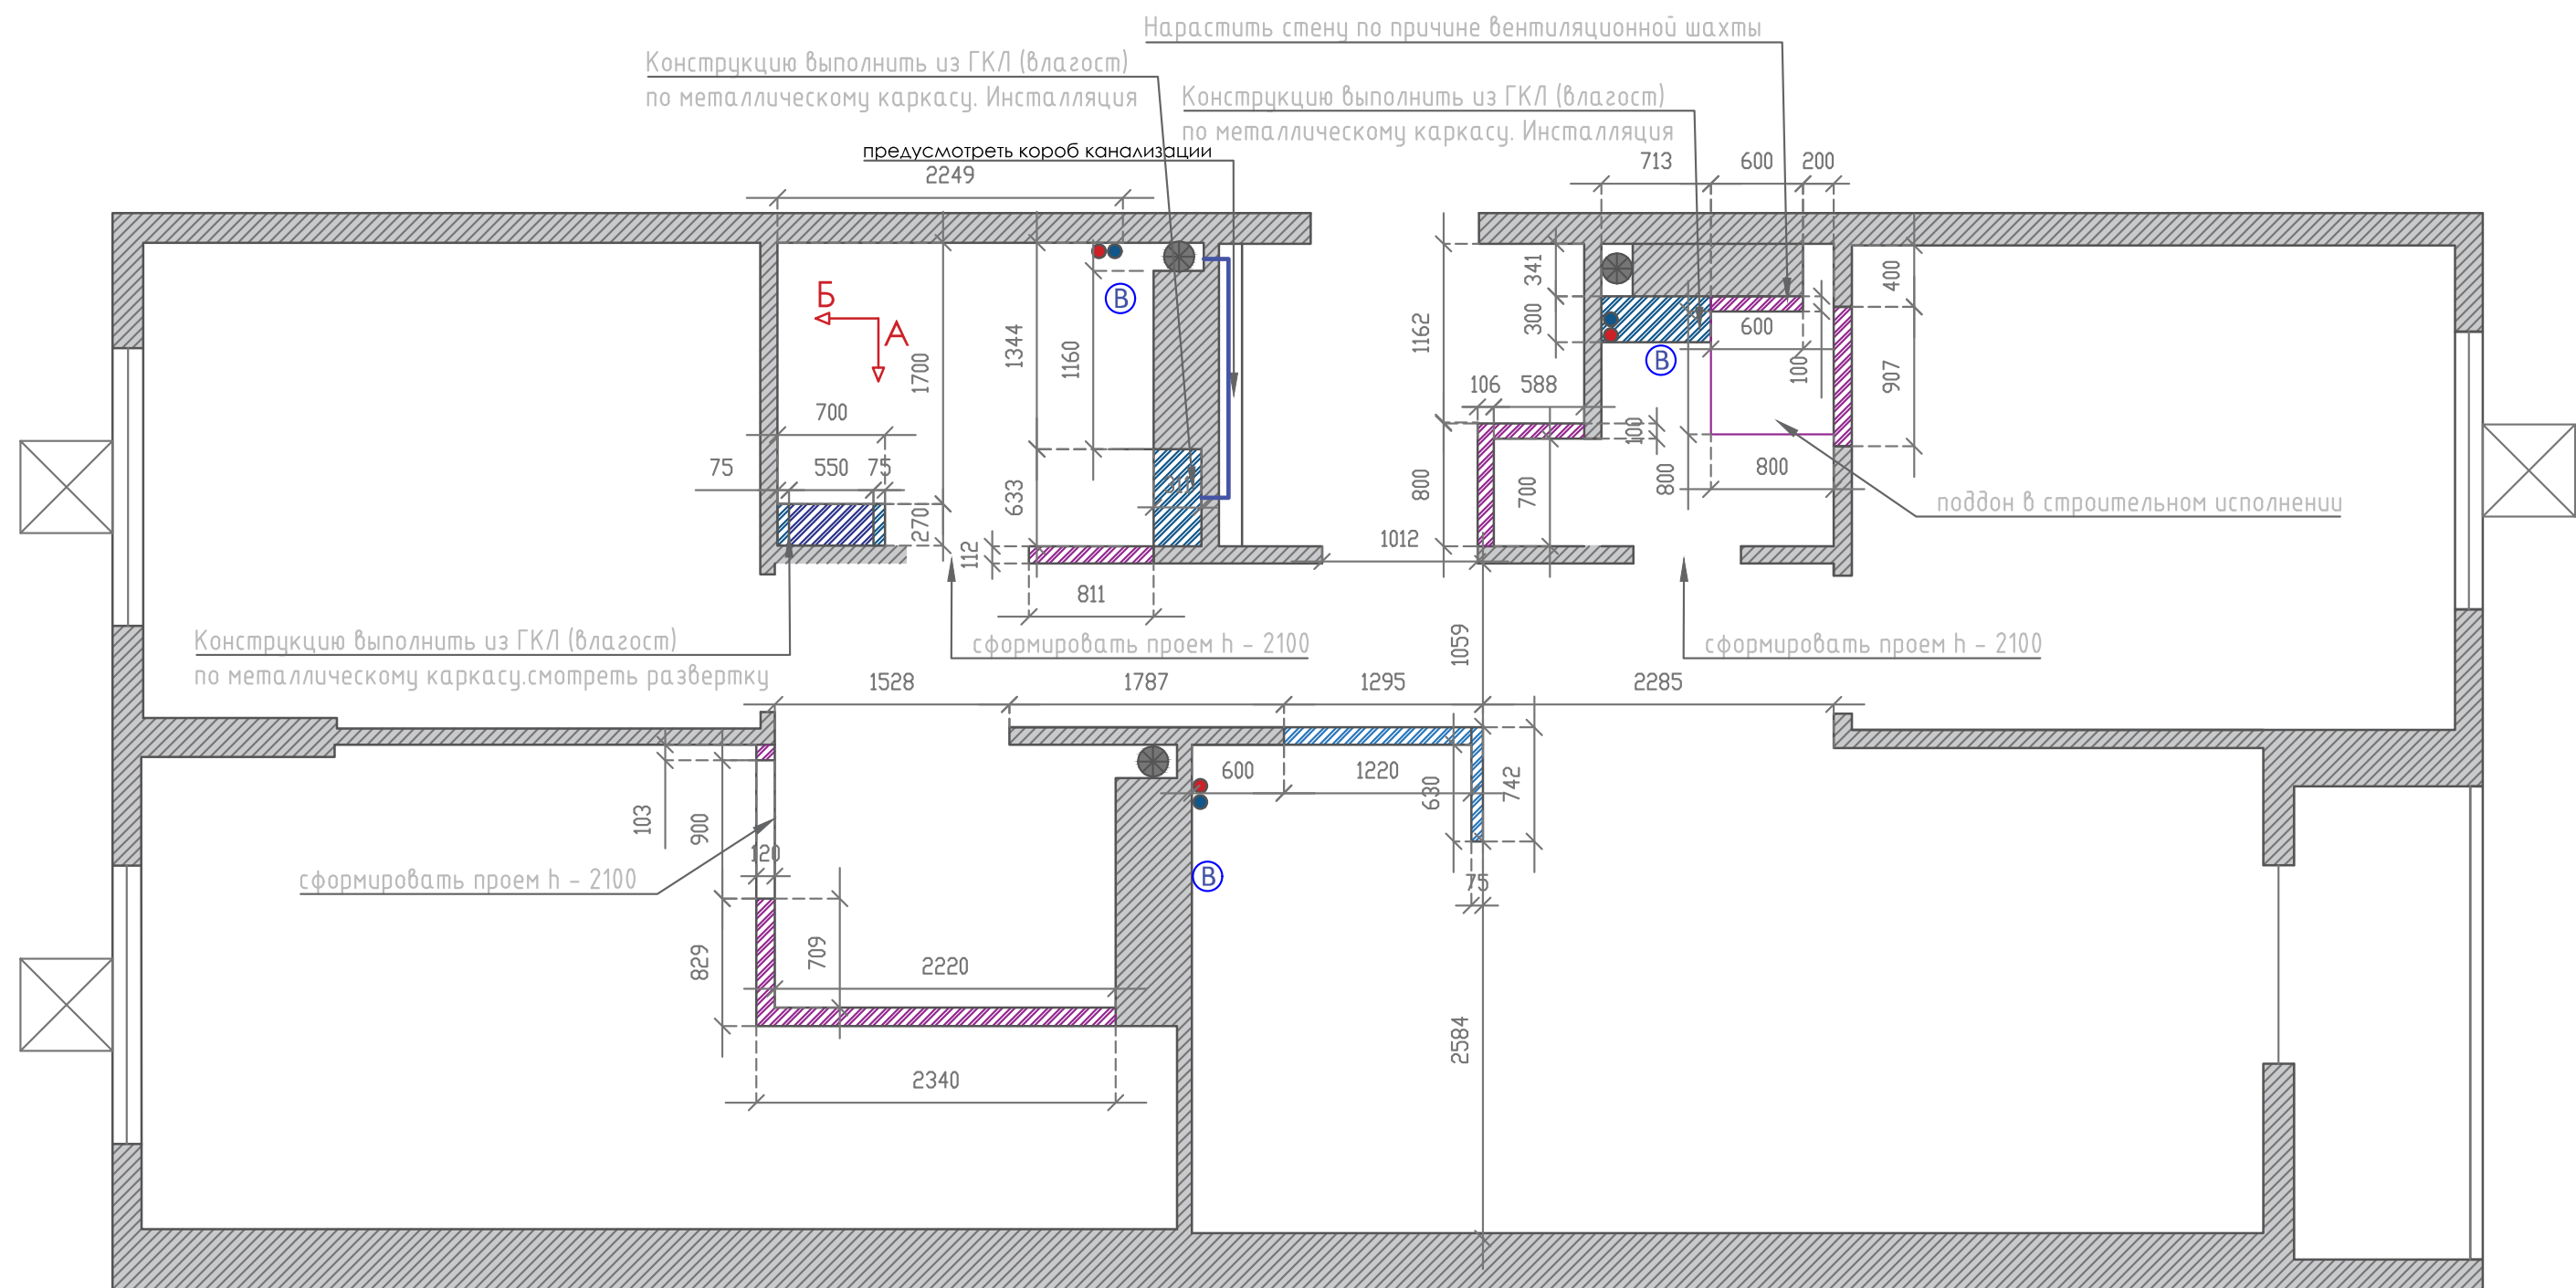

Возводимые перегородки посчитано без учета запаса

	Возводимые перегородки (газоблок)
	Возводимые перегородки (гипсокартон)

		Подпись	Дата	Дизайн - проект квартиры	Стадия	Лист	
					ДП	3	
				Монтаж перегородок			