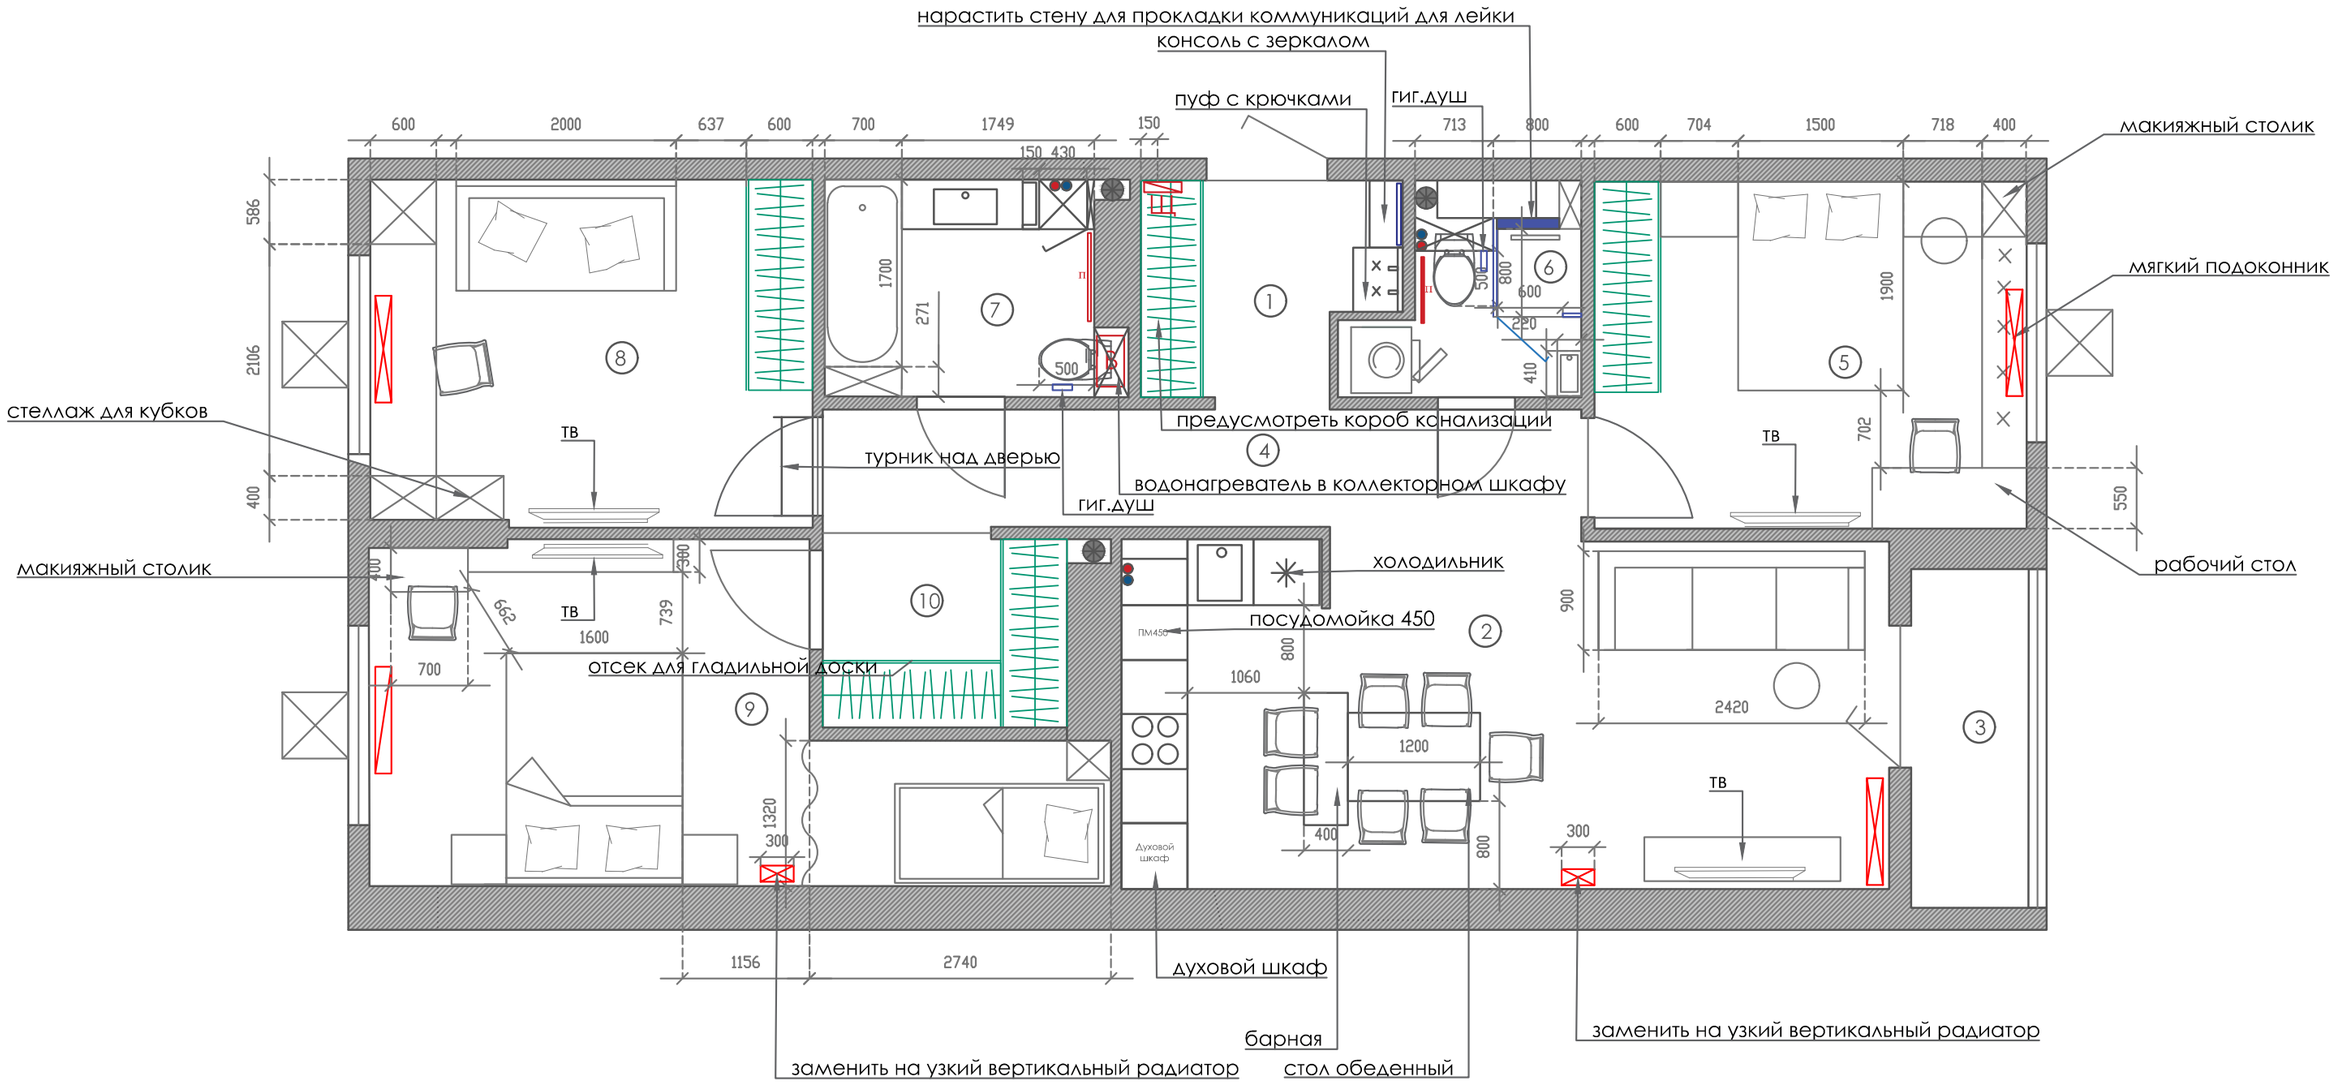


Экспликация помещений

1	Прихожая	4,3м2
2	Кухня - Гостиная	22,15м2
3	Лоджия	3,4м2
4	Коридор	7,93м2
5	Комната девочки	12,5м2
6	Санузел	2,7м2
7	Ванна	5,14м2
8	Комната мальчика	12,66м2
9	Спальня	16,1м2
10	холл	3,97м2

Общая площадь - 91,88 м2 Н потолков - 2785мм

Условные обозначения

канализация

ГВС-ХВС

		Подпись	Дата	Дизайн - проект квартиры	Стадия	Лист	
					ДП	5	
	ИНТЕРЬЕР студия дизайна			План расстановки мебели и оборудования			