


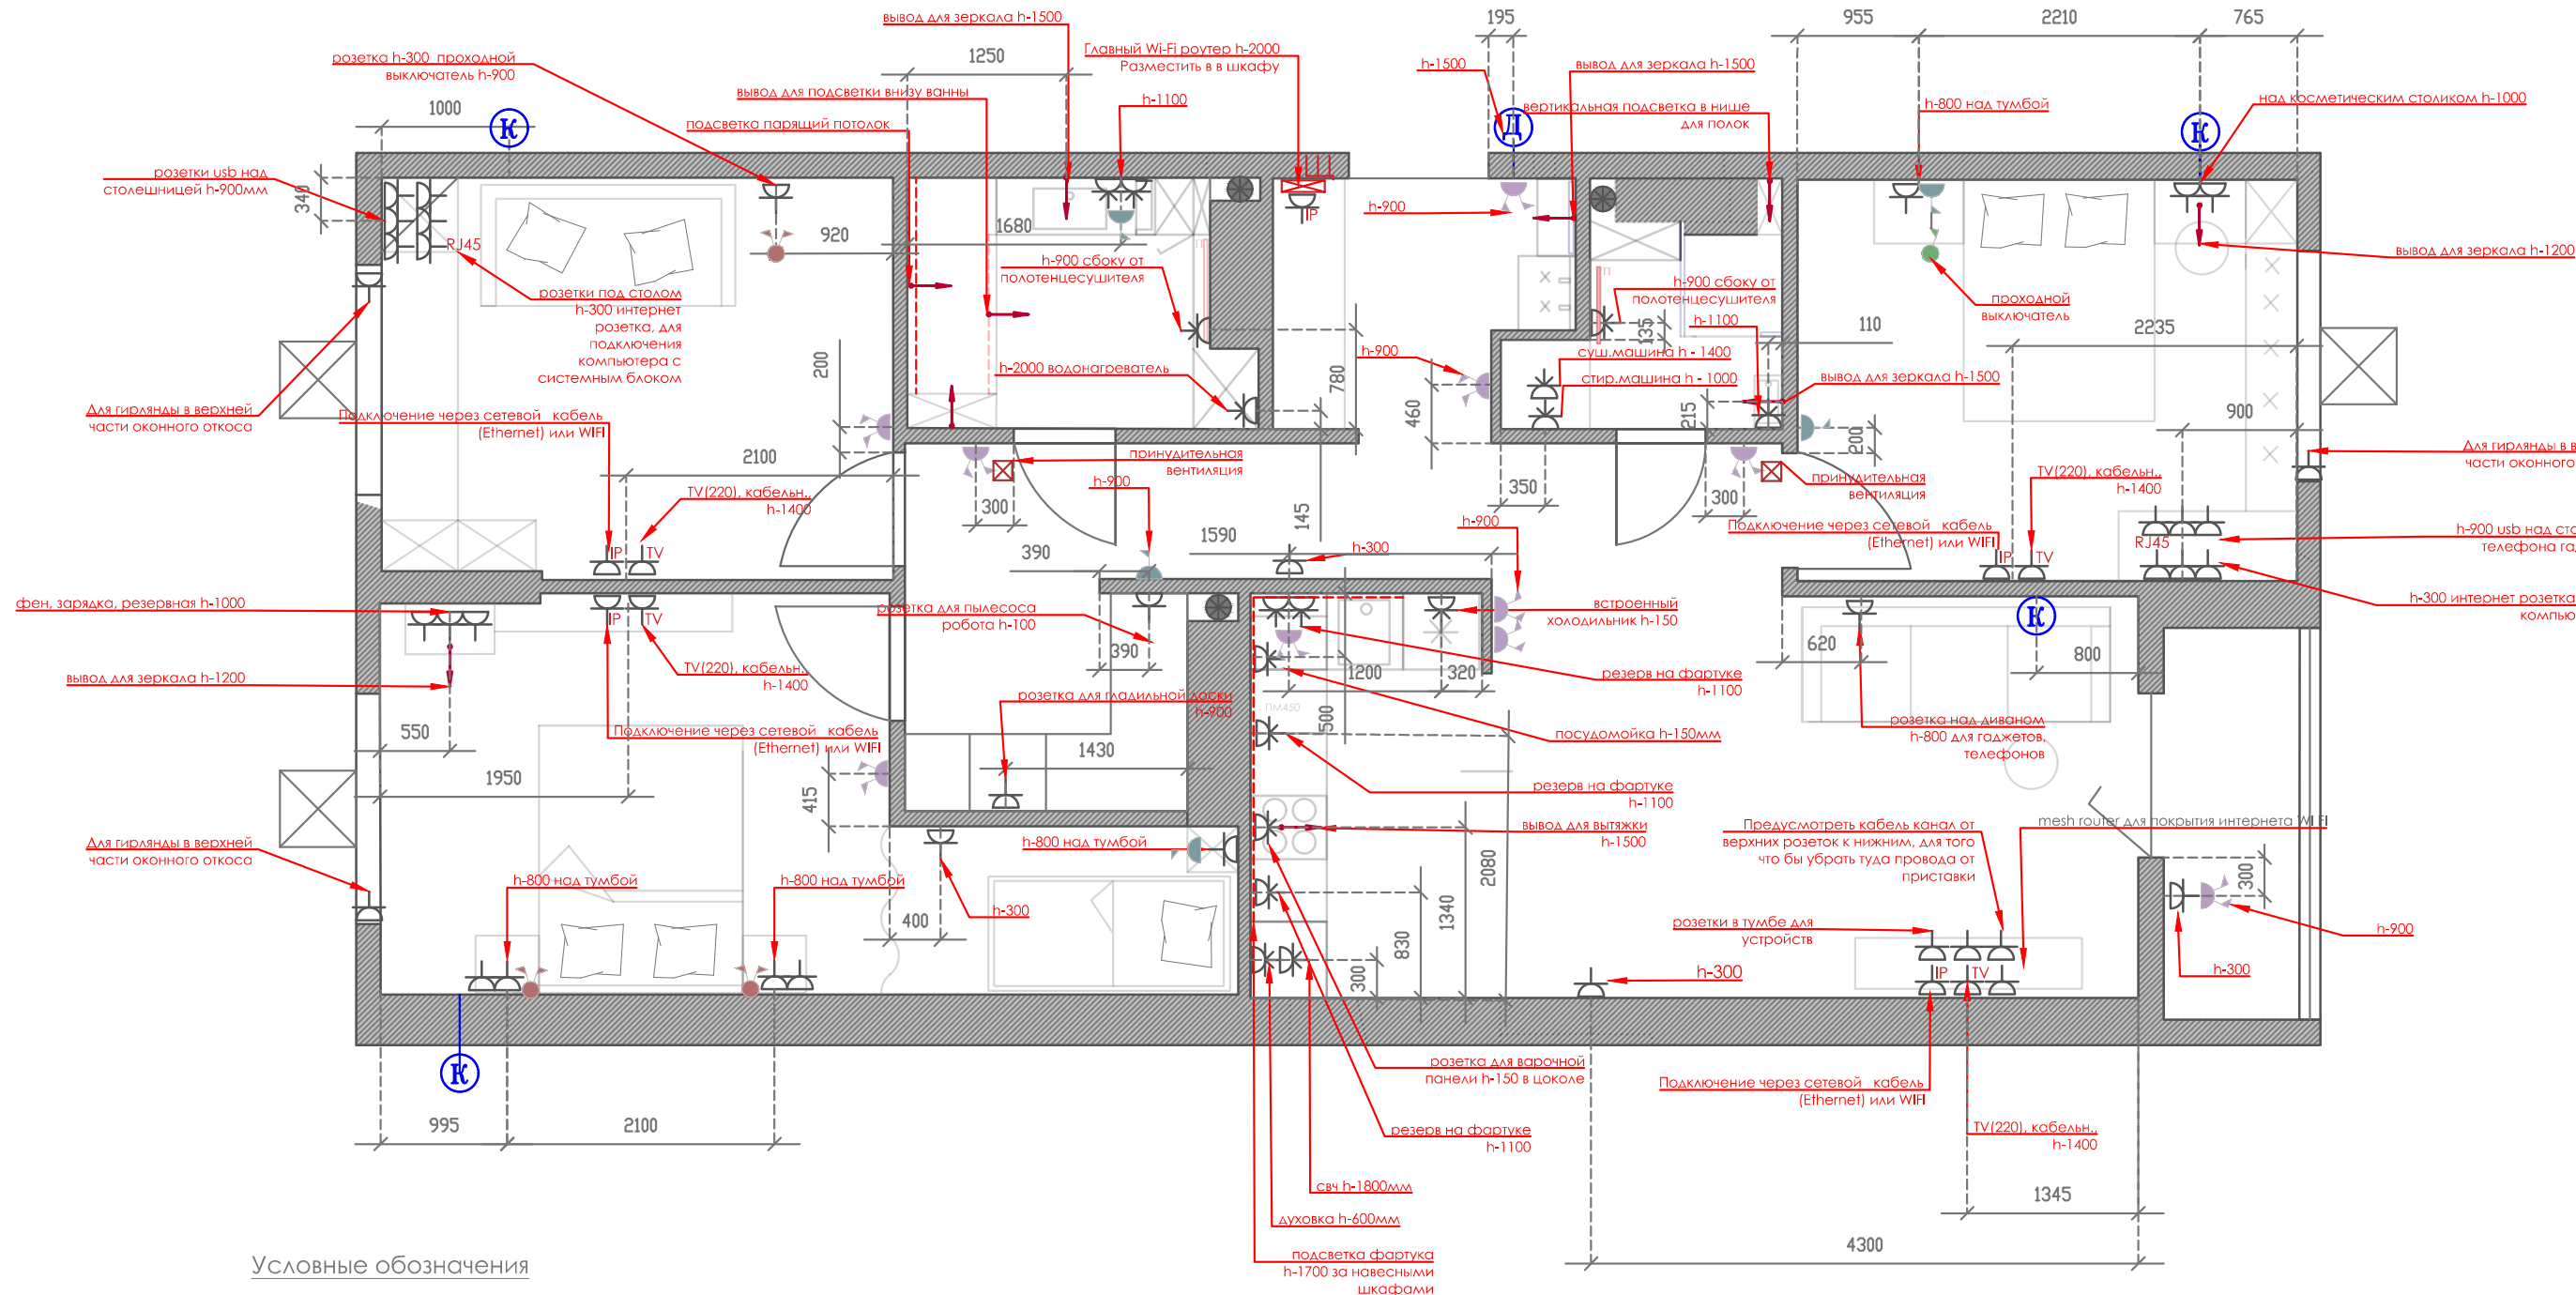

Условные обозначения

	Розетка электрическая		Регулятор тёплого пола
	Розетка влагозащищённая		Домофон
	Интернет-розетка		Принудительная вентиляция
	Интернет, телефон		Кондиционер
	Эл.вывод		Выключатель одноклавишный
	Телевизионная розетка		Выключатель двухклавишный
	Выключатель проходной		Выключатель проходной двухклавишный

Примечания:
1. Высоту электророзеток принять 300мм от чистого пола,высоту выключателей принять 900мм от чистого пола если иное не указано в чертежах
2. Расположение телевизионных розеток уточнить в зависимости от TV блока
3. Для электровыводов дать запас провода не менее 500мм
4. В санузлах предусмотреть датчик от протечки Neptun
5. Размеры и площади даны без учёта отделки стен
6. Все высоты в плане даны от уровня "чистого пола"
7. Точная привязка розеток и выводов на кухне уточняется и корректируется после выбора конкретной модели кухни!!!

		Подпись	Дата	Дизайн - проект квартиры	Стадия	Лист	
					ДП	6	
				Схема расположения розеток и выключателей			